



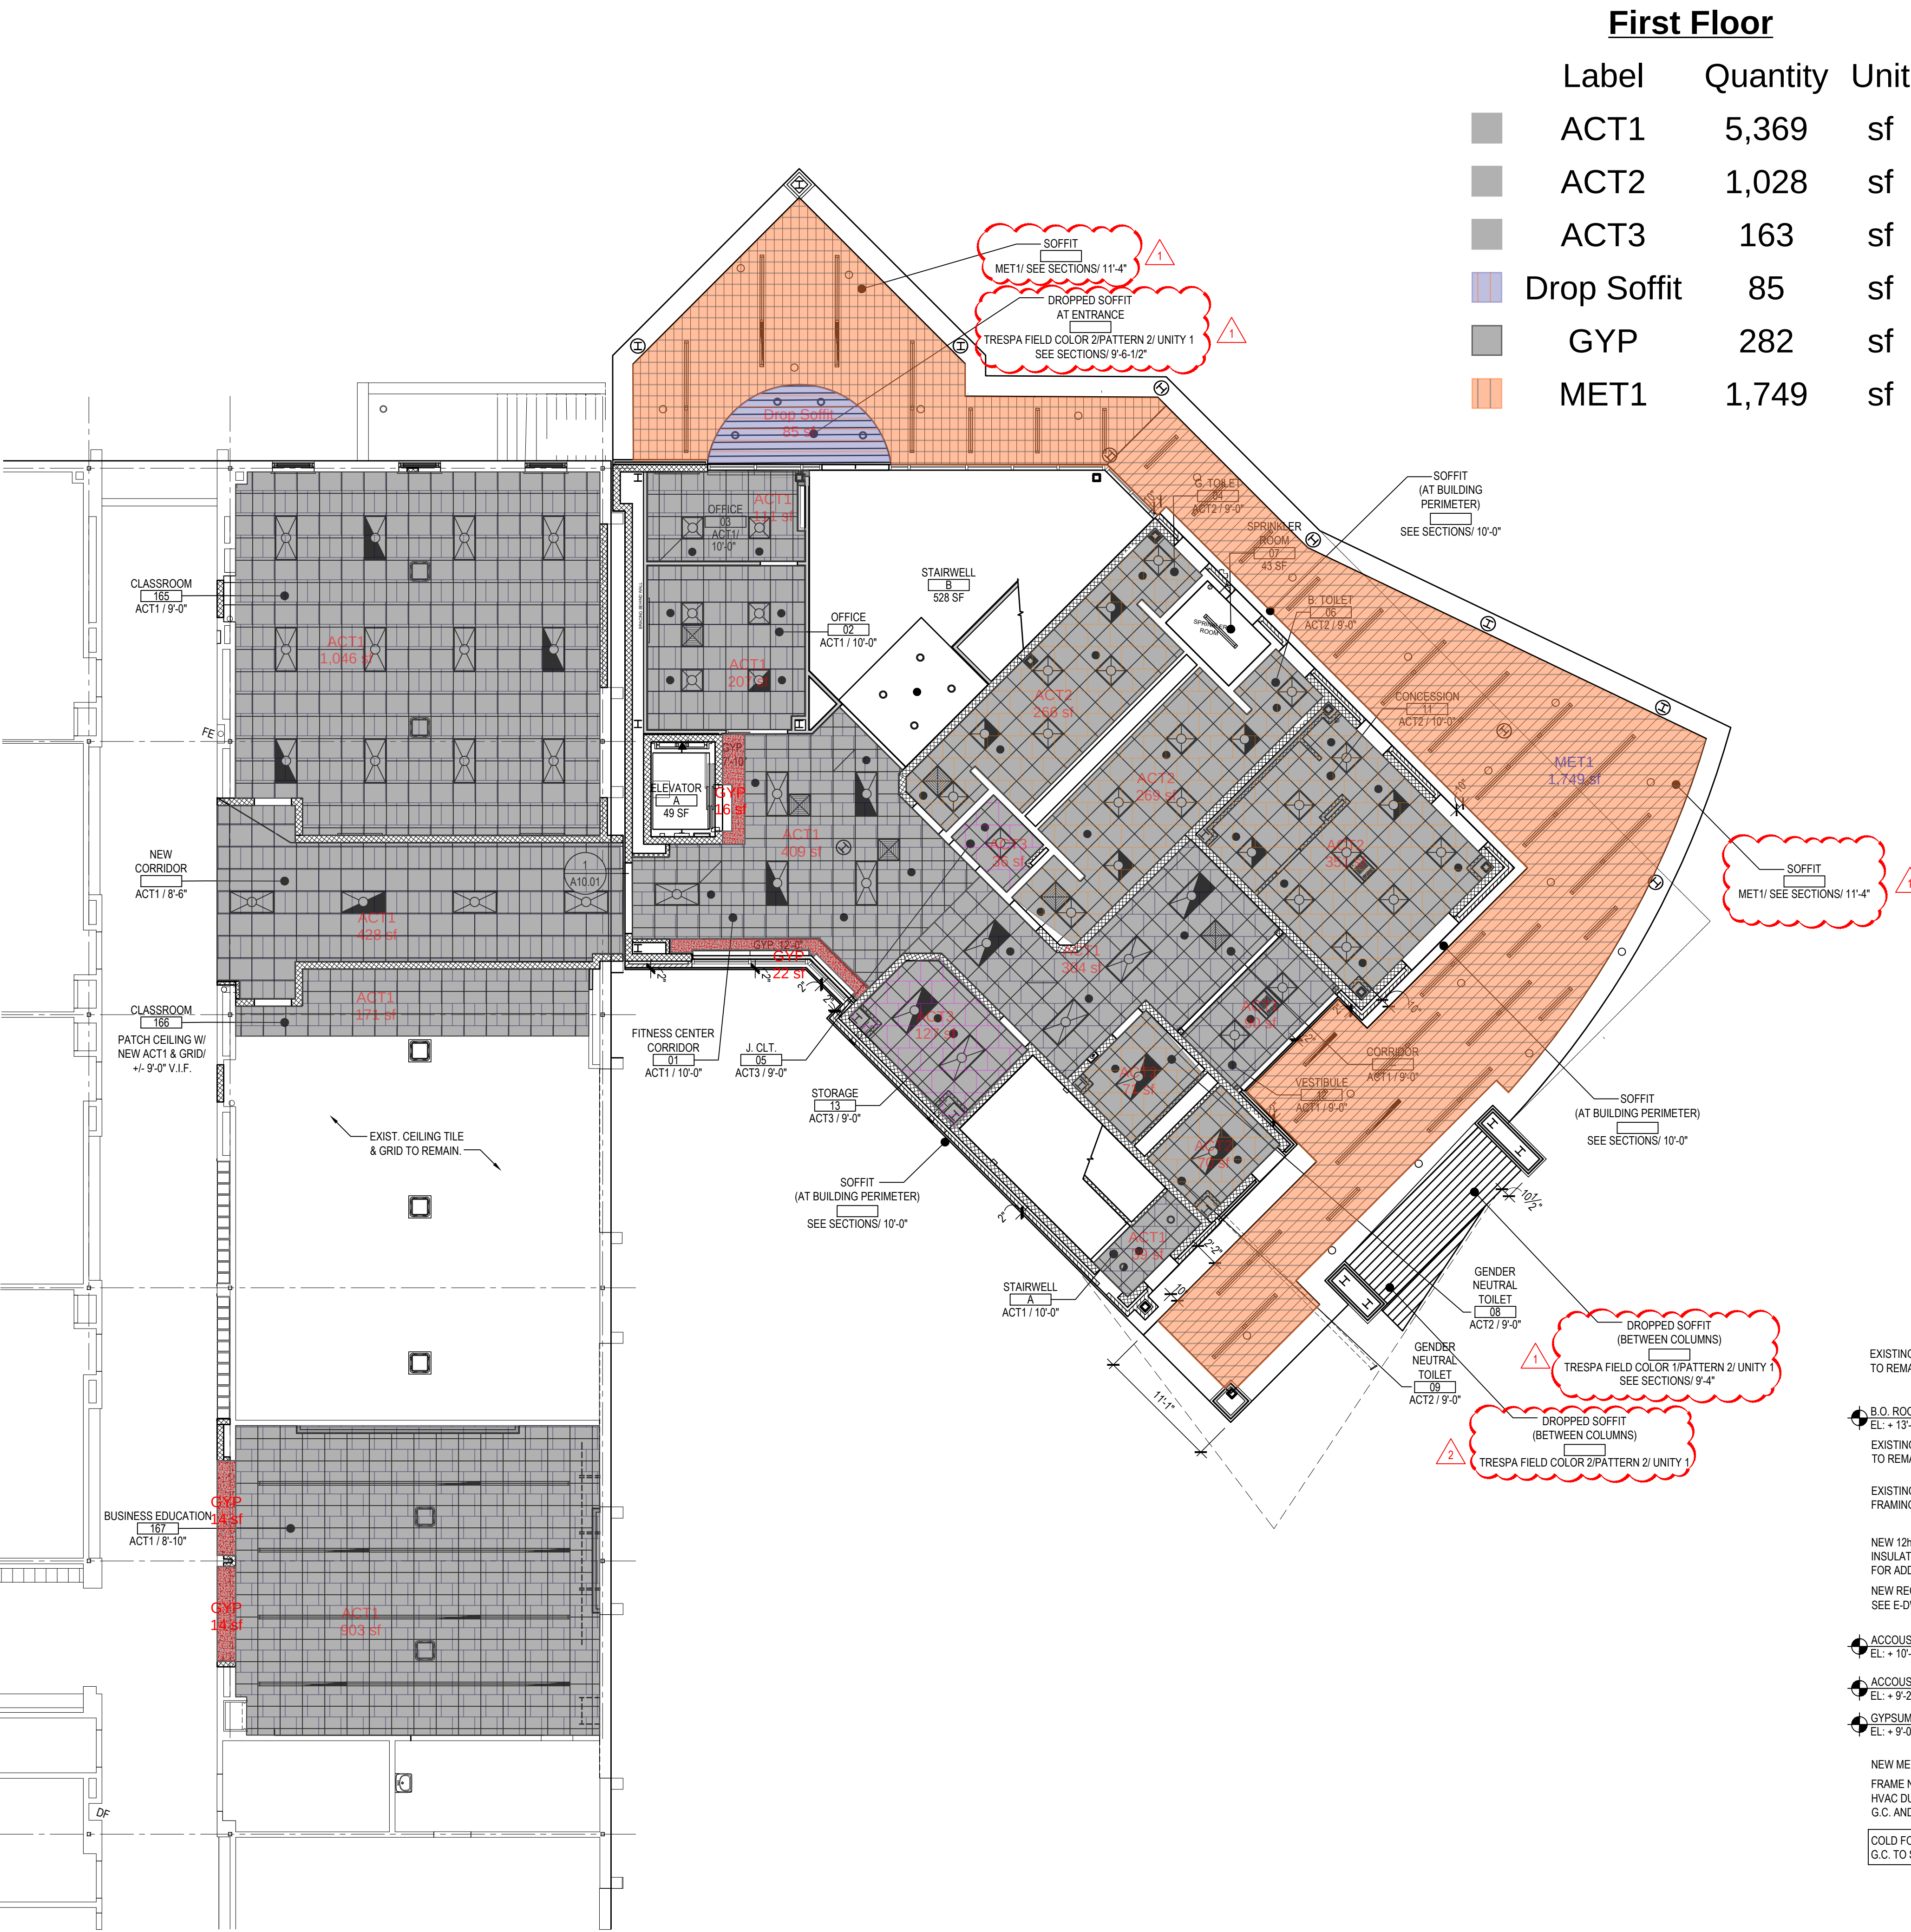

PARTIAL FIRST FLOOR REFLECTED CEILING PLAN - CLASSROOM 165, CLASSROOM 167, BUSINESS EDUCATION 167 & FITNESS CENTER

NOTE:


SCALE: 1/8" = 1'-0"

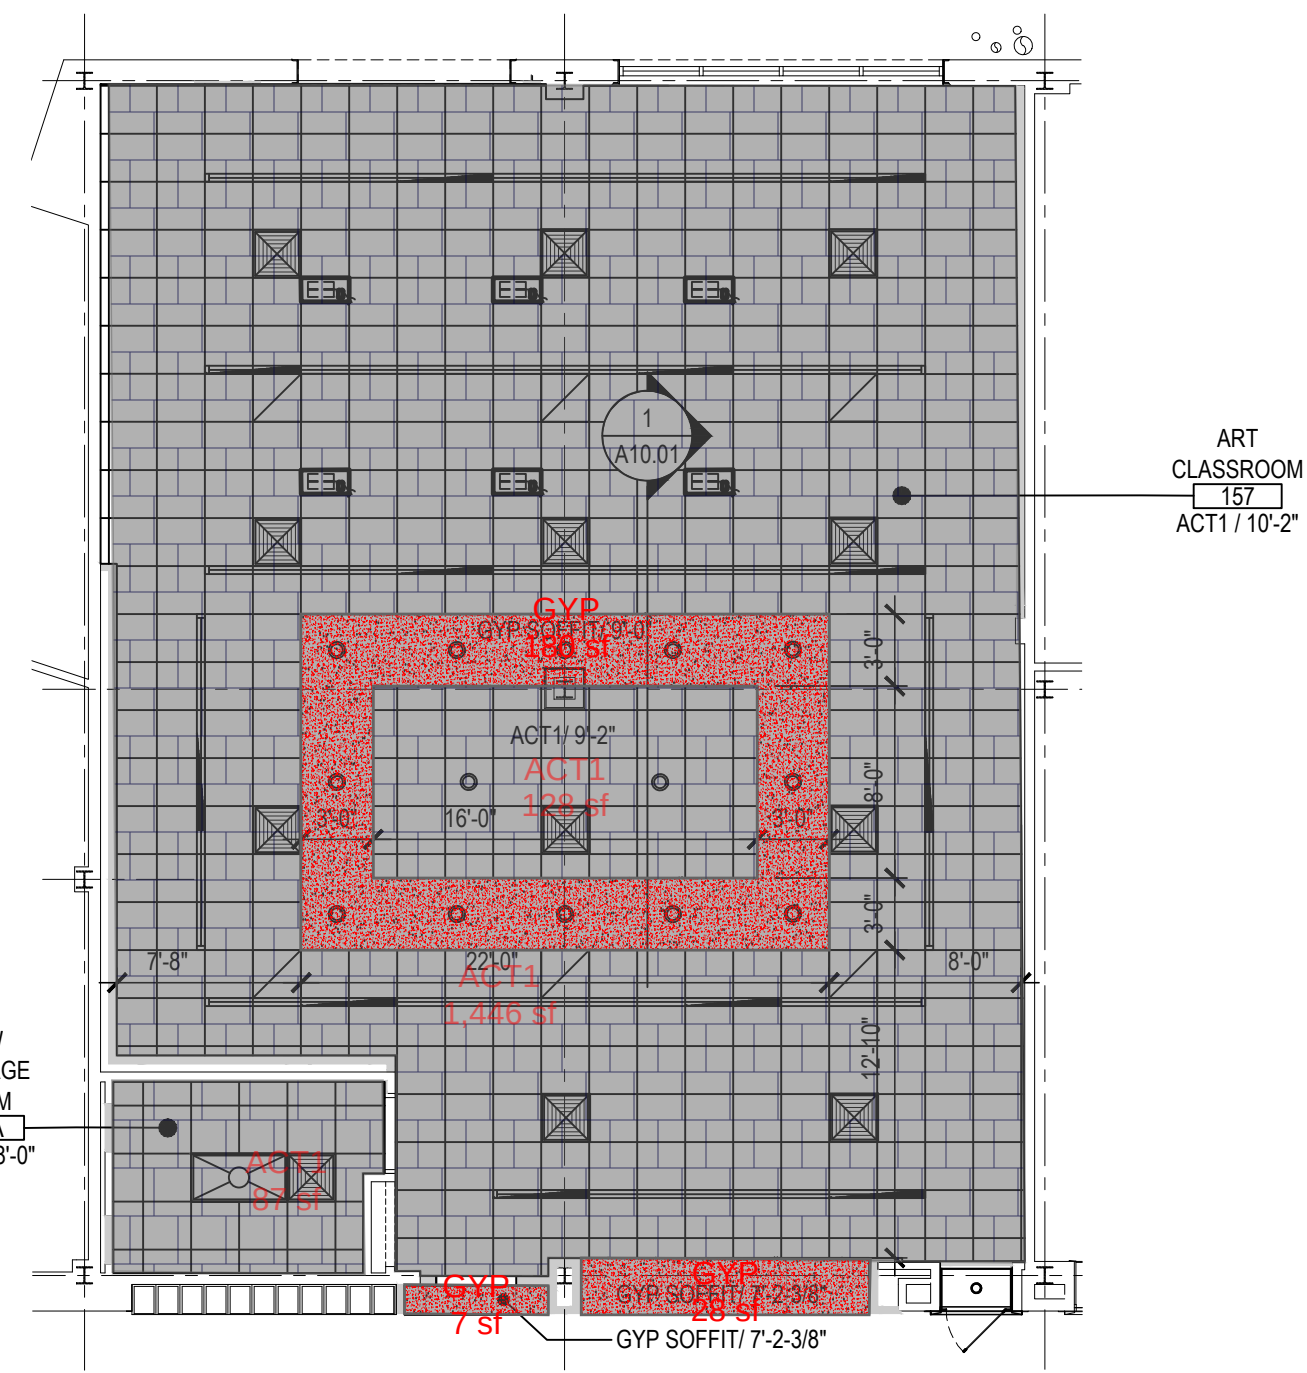

PARTIAL FIRST FLOOR REFLECTED CEILING PLAN - ART CLASSROOM 157

NOTE:


SCALE: 1/8" = 1'-0"

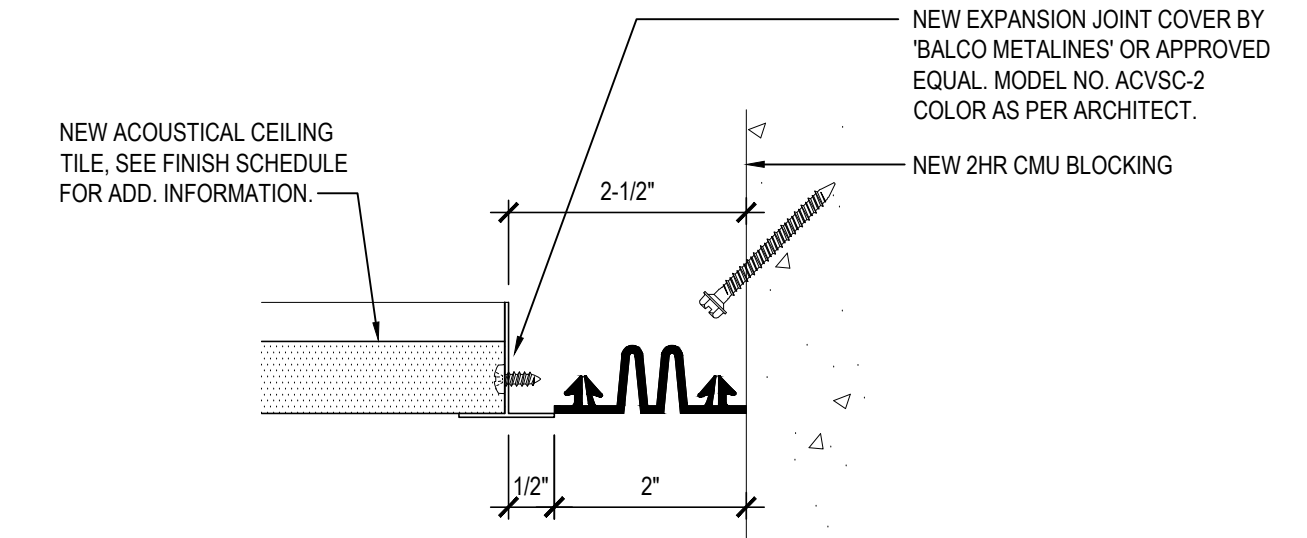

1 ACOUSTICAL CEILING TO WALL EXPANSION JOINT

NOTE:

SCALE: 6" = 1'-0"

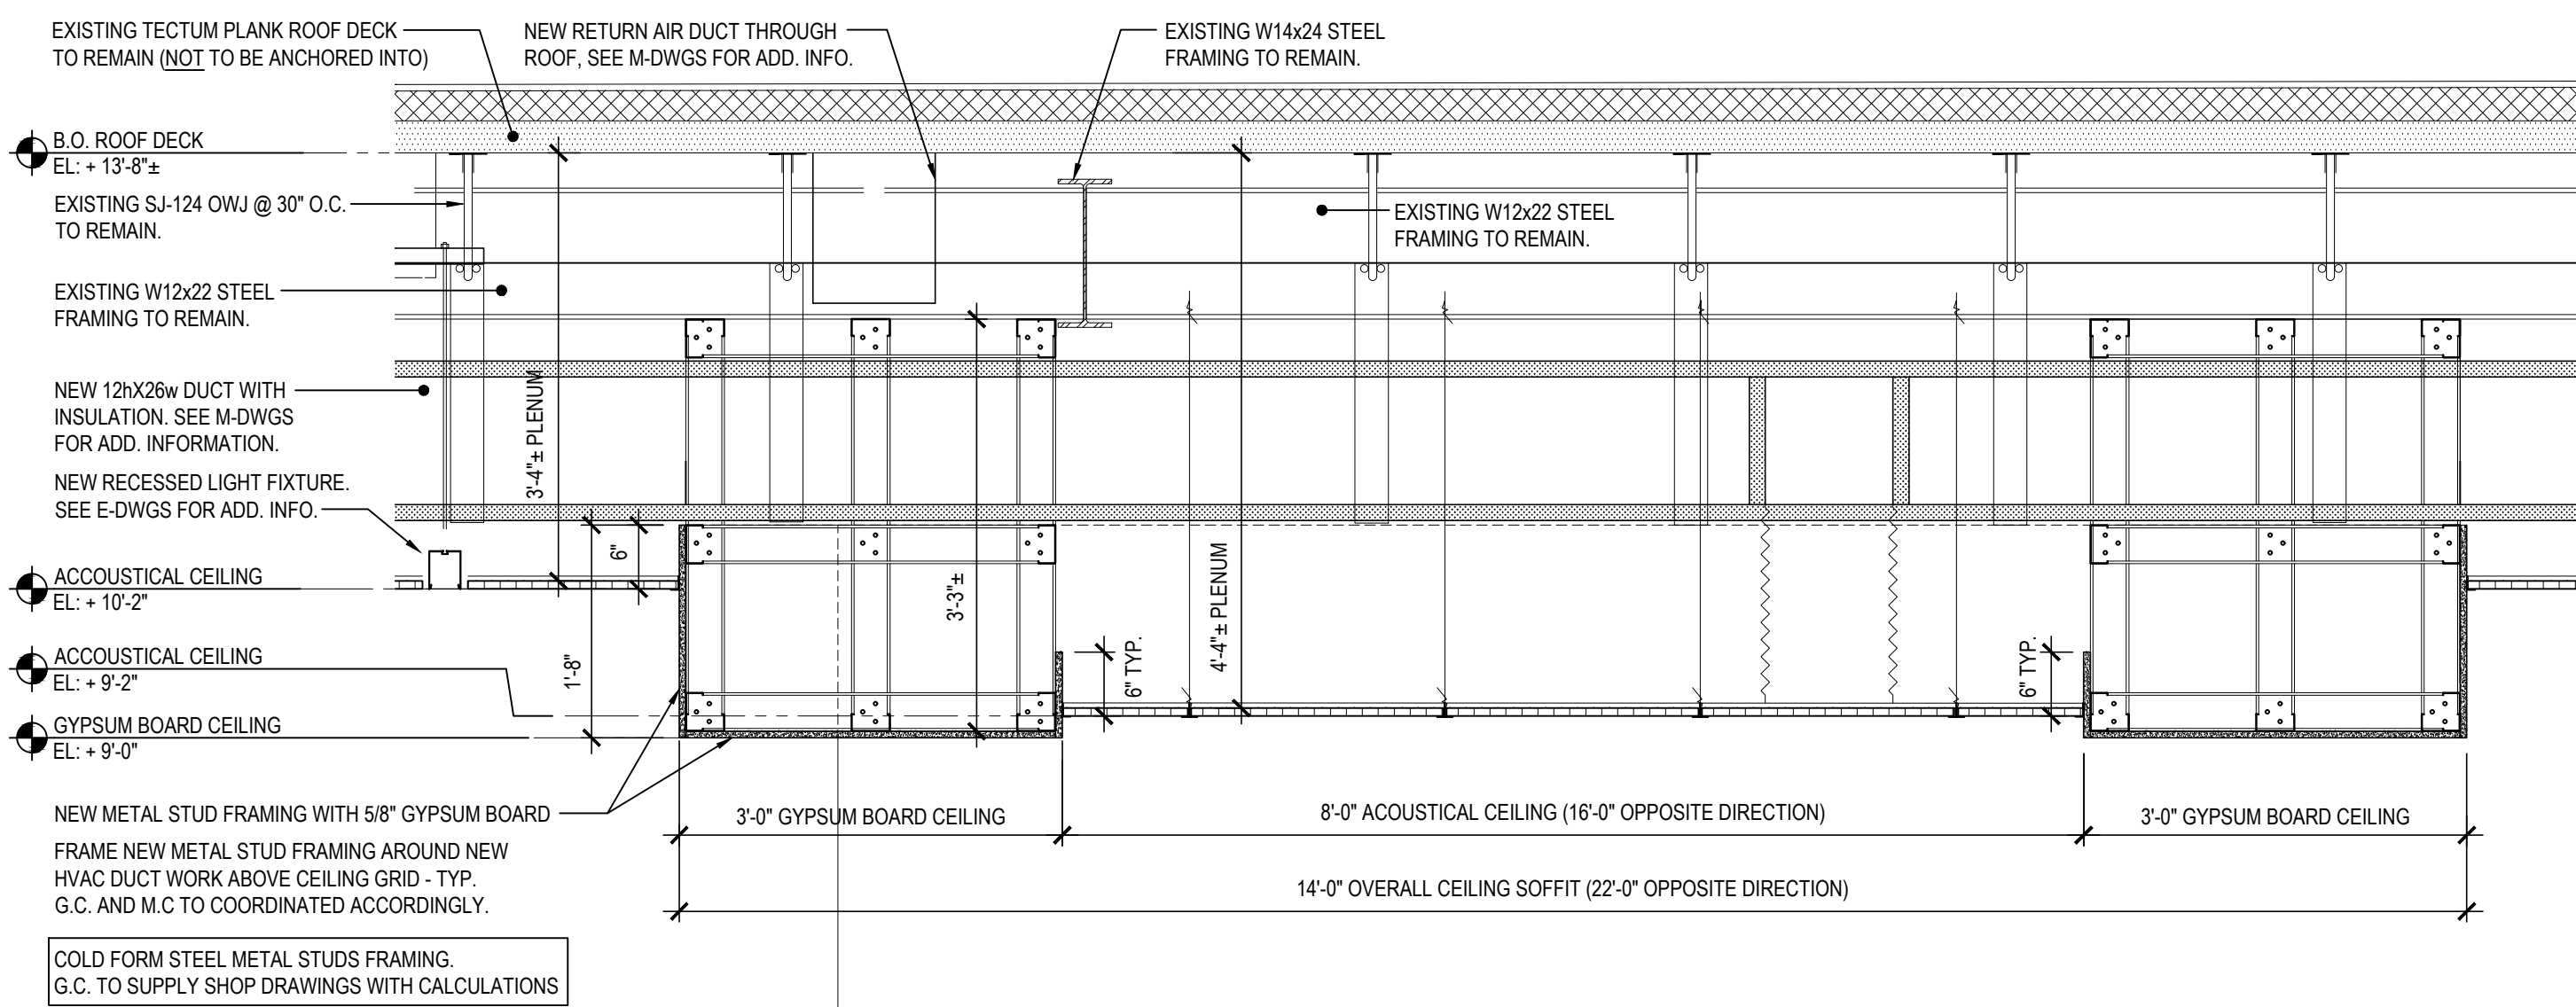

1 CEILING SOFFIT @ ART CLASSROOM 157

NOTE: SEE DRAWING A9.01 FOR ADDITIONAL INFORMATION.

SCALE: 3/4" = 1'-0"


SYMBOLS LEGEND	
SYMBOL	DESCRIPTION
	ROOM TAG, CEILING TILE TYPE AND FINISH CEILING ELEVATION (A.F.F.)
	NO CLG. OPEN TO STRUCTURE AND DECK ABOVE (PAINT)
	SUSPENDED ACOUSTICAL CEILING TILE AND GRID
	GYPSUM BOARD SOFFIT OVER METAL FRAMING. REFER TO DETAIL, THIS SHEET. TAPE, SPACKLE AND PAINT.
	HIGH PRESSURE LAMINATE (HPL) ARCHITECTURAL CLADDING -TRESPA 5/16" SPECTRUM UNITY PLANK. SEE A-6 SERIES DWGS FOR ADD. INFO.
	RECESSED OR SURFACE MOUNTED LIGHT FIXTURE BY E.C. REFER TO E-SERIES DRAWINGS.
	EXIT SIGN BY E.C. REFER TO E-SERIES DRAWINGS.
	CEILING MOUNTED SPEAKER BY E.C. REFER TO E-SERIES DRAWINGS.
	SMOKE / HEAT DETECTORS BY E.C. REFER TO E-SERIES DRAWINGS.
	OCCUPANCY SENSOR BY E.C. REFER TO E-SERIES DRAWINGS.
	CEILING GRILLE / REGISTER BY M.C. REFER TO M-SERIES DRAWINGS.
	NEW CASSETTE TYPE AIR CONDITIONING UNIT BY M.C. REFER TO M-SERIES DRAWINGS.
	HVAC DUCT WORK BY M.C. REFER TO M-SERIES DRAWINGS.
	NEW CORD REEL AND PLENUM BOX BY E.C. PLENUM BOX MUST BE COORDINATED WITH NEW CEILING SYSTEM AND G.C. COORDINATE BOX LOCATION WITH BUILDING STEEL. SEE DETAIL 3/E7.01 FOR ADD. INFO.
	EXTERIOR WALL MOUNTED LIGHT FIXTURE BY E.C. REFER TO E-SERIES DRAWINGS.
	CEILING MOUNTED CABINET HEATER BY M.C. REFER TO M-SERIES DRAWINGS.
	NEW SPRINKLER HEADS. REFER TO SP-SERIES DRAWINGS FOR ADD. INFO.
	REVISION CLOUD AND KEYED DESIGNATION. REFER TO DRAWING TITLE BLOCK FOR ADDITIONAL INFORMATION.

TYPICAL REFLECTED CEILING PLAN NOTES

1. CEILING PLANS MAY NOT INDICATE ALL MECHANICAL AND / OR ELECTRICAL CEILING MOUNTED ITEMS. REFER TO M - SERIES AND E - SERIES DRAWINGS FOR ADDITIONAL INFORMATION.
2. CEILING GRID SHALL BE ARRANGED TO BE SPACED EQUALLY IN EACH DIRECTION WITH NO TILE LESS THAN 6" UNLESS OTHERWISE REQUIRED.
3. PROVIDE CEILING EXPANSION JOINT AT ALL NEW TO EXISTING INTERSECTIONS AND WHERE INDICATED ON PLANS.
4. UNLESS OTHERWISE NOTED, ALL SOFFITS AND WINDOW POCKETS SHALL BE 3/4" TYPE 'X' GYP. BOARD OVER 18 GA. COLD FORMED FRAMING AT 16" O.C.
5. ALL AREAS NOTED AS 'OPEN' AND / OR 'NO CEILING (CLG.) SHALL BE PAINTED - INCLUDING BUT NOT LIMITED TO DECK, STRUCTURE, DUCTWORK, ETC.)
6. ACOUSTICAL CEILINGS SHALL HAVE A FLAME SPREAD OF 25 OR LESS COMPLYING WITH 'ASTM E-84'; SMOKE DEVELOPED RATING OF 80 OR LESS COMPLYING WITH PERFORMANCE REQUIREMENTS AND PHYSICAL CHARACTERISTICS OF THE SPECIFIED CEILINGS AS INDICATED IN THE REFLECTED CEILING PLAN. (ASTM E-1284)
7. ACOUSTICAL CEILINGS SHALL HAVE A MINIMUM NOISE REDUCTION COEFFICIENT (NRC) RATING OF 0.65.

REV.	DATE	ITEM
01	03/20/25	BID ADD. NO. 01
02	03/28/25	BID ADD. NO. 02

NOTICE
THESE DRAWINGS ARE BASED ON CONSTRUCTION DRAWINGS NOT PREPARED BY BBS ARCHITECTS, LANDSCAPE ARCHITECTS AND ENGINEERS, P.C. AND, THEREFORE, MAY NOT REPRESENT THE CONDITIONS AS CONSTRUCTED AT THE TIME. ALL EXISTING INFORMATION SHOWN ARE REPRESENTED AS SUGGESTIVE INFORMATION AS THEY HAVE NOT BEEN BUILT AND DETAIL PER THE ORIGINAL DOCUMENTS OR PER THE OWNER'S INFORMATION.

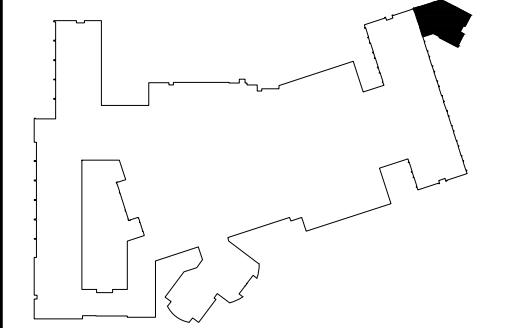

KEY PLAN
NOT TO SCALE

GARDEN CITY UNION FREE SCHOOL DISTRICT
ADDITIONS AND ALTERATIONS
GARDEN CITY HIGH SCHOOL
GARDEN CITY, NASSAU COUNTY, NEW YORK


PROJECT
DRAWING BY: WCA
CHECK BY: GWS

NOTICE
THIS DRAWING, PREPARED FOR THE SPECIFIC PROJECT INDICATED IS AN INSTRUMENT OF SERVICE, AND THE PROPERTY OF BBS ARCHITECTS, LANDSCAPE ARCHITECTS AND ENGINEERS, P.C. NO REPRODUCTION OR ANY USE OF THIS DRAWING FOR ANY OTHER PROJECT IS PROHIBITED. ANY ALTERATION OR REPRODUCTION OF THIS DOCUMENT IS ALSO PROHIBITED WITHOUT THE WRITTEN CONSENT OF THE ARCHITECT OR ENGINEER.

BBS
ARCHITECTS
LANDSCAPE ARCHITECTS
ENGINEERS
244 EAST MAIN STREET
PATCHOGUE
NEW YORK 11772
T. 631.475.0349
F. 631.475.0361
187 WOLF ROAD, STE. 205
ALBANY
NEW YORK 12205
T. 518.621.7650
F. 518.621.7655
www.BBSARCHITECTURE.com

SED No: 28-02-18-03-0-007-034
DISTRICT: GARDEN CITY UNION FREE SCHOOL DISTRICT
PROJECT: GARDEN CITY HIGH SCHOOL ADDITIONS AND ALTERATIONS
DWG TITLE: PARTIAL FIRST FLR REFLECTED CEILING PLANS
SCALE: AS NOTED
DATE: MARCH 6, 2025
BID PICK-UP: MARCH 6, 2025
FILE No: 24-145


A10.01

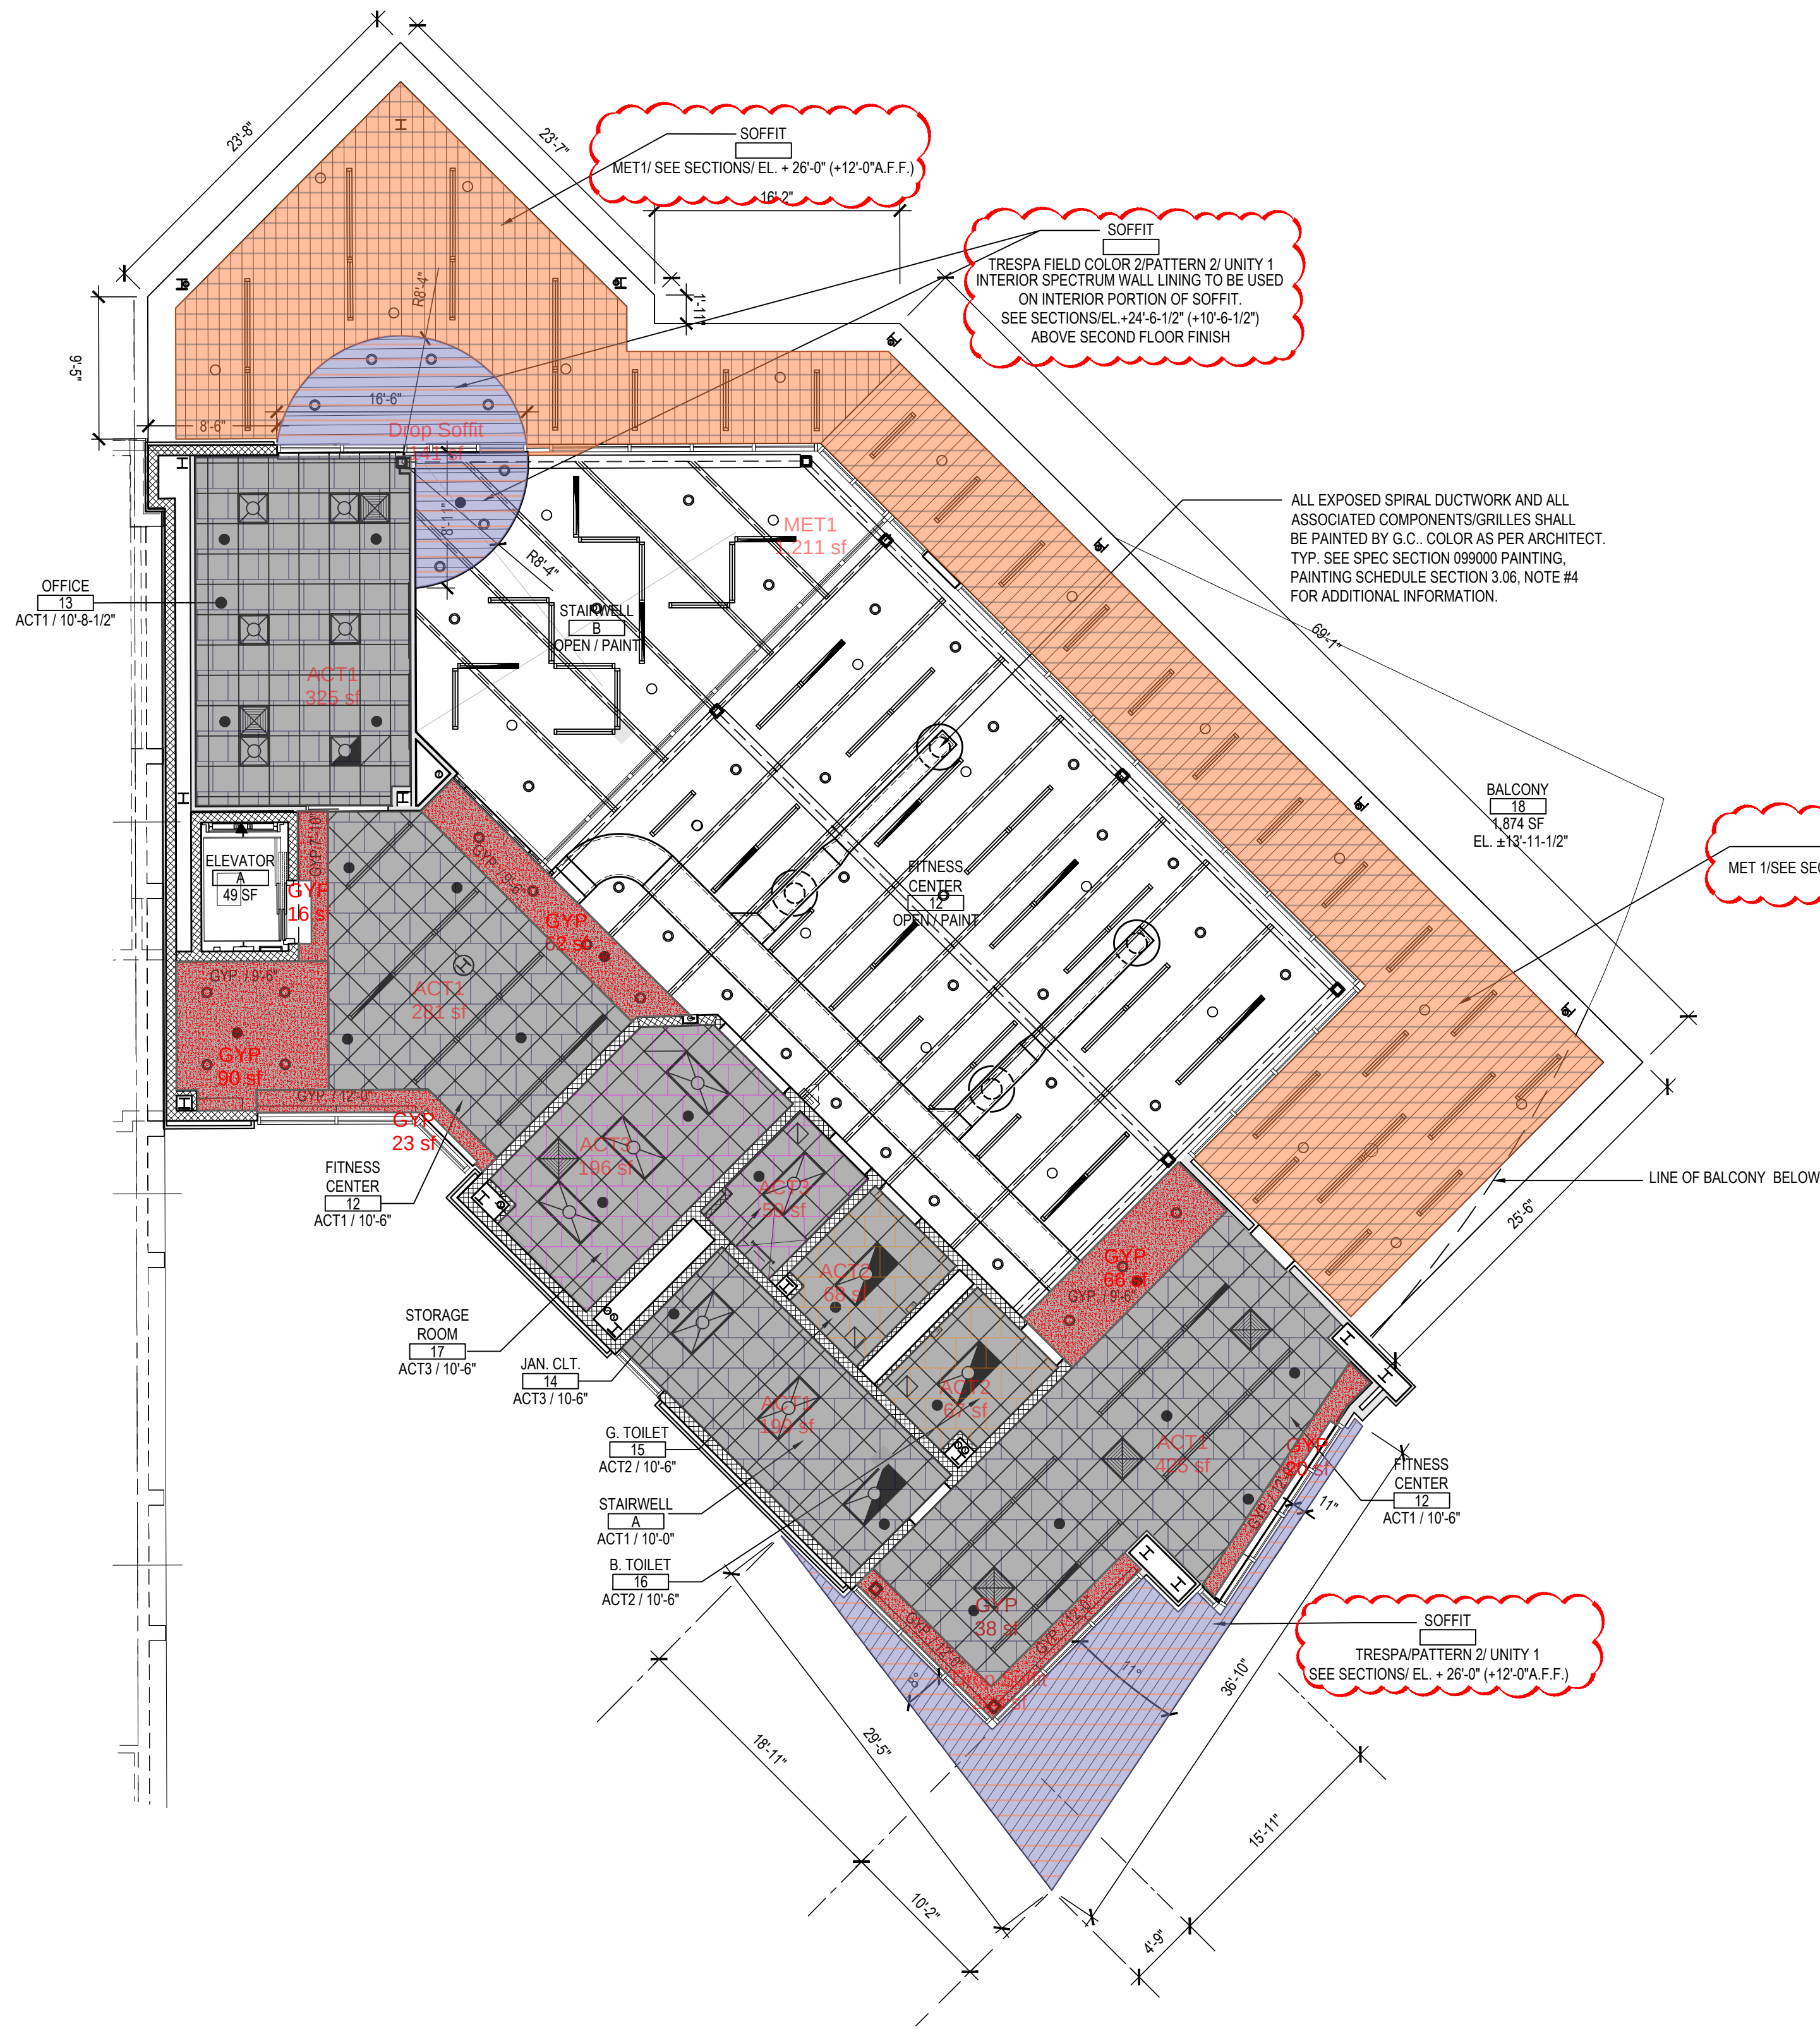

PARTIAL SECOND FLOOR REFLECTED CEILING PLAN - FITNESS CENTER

NOTE:

SCALE: 1/8" = 1'-0"

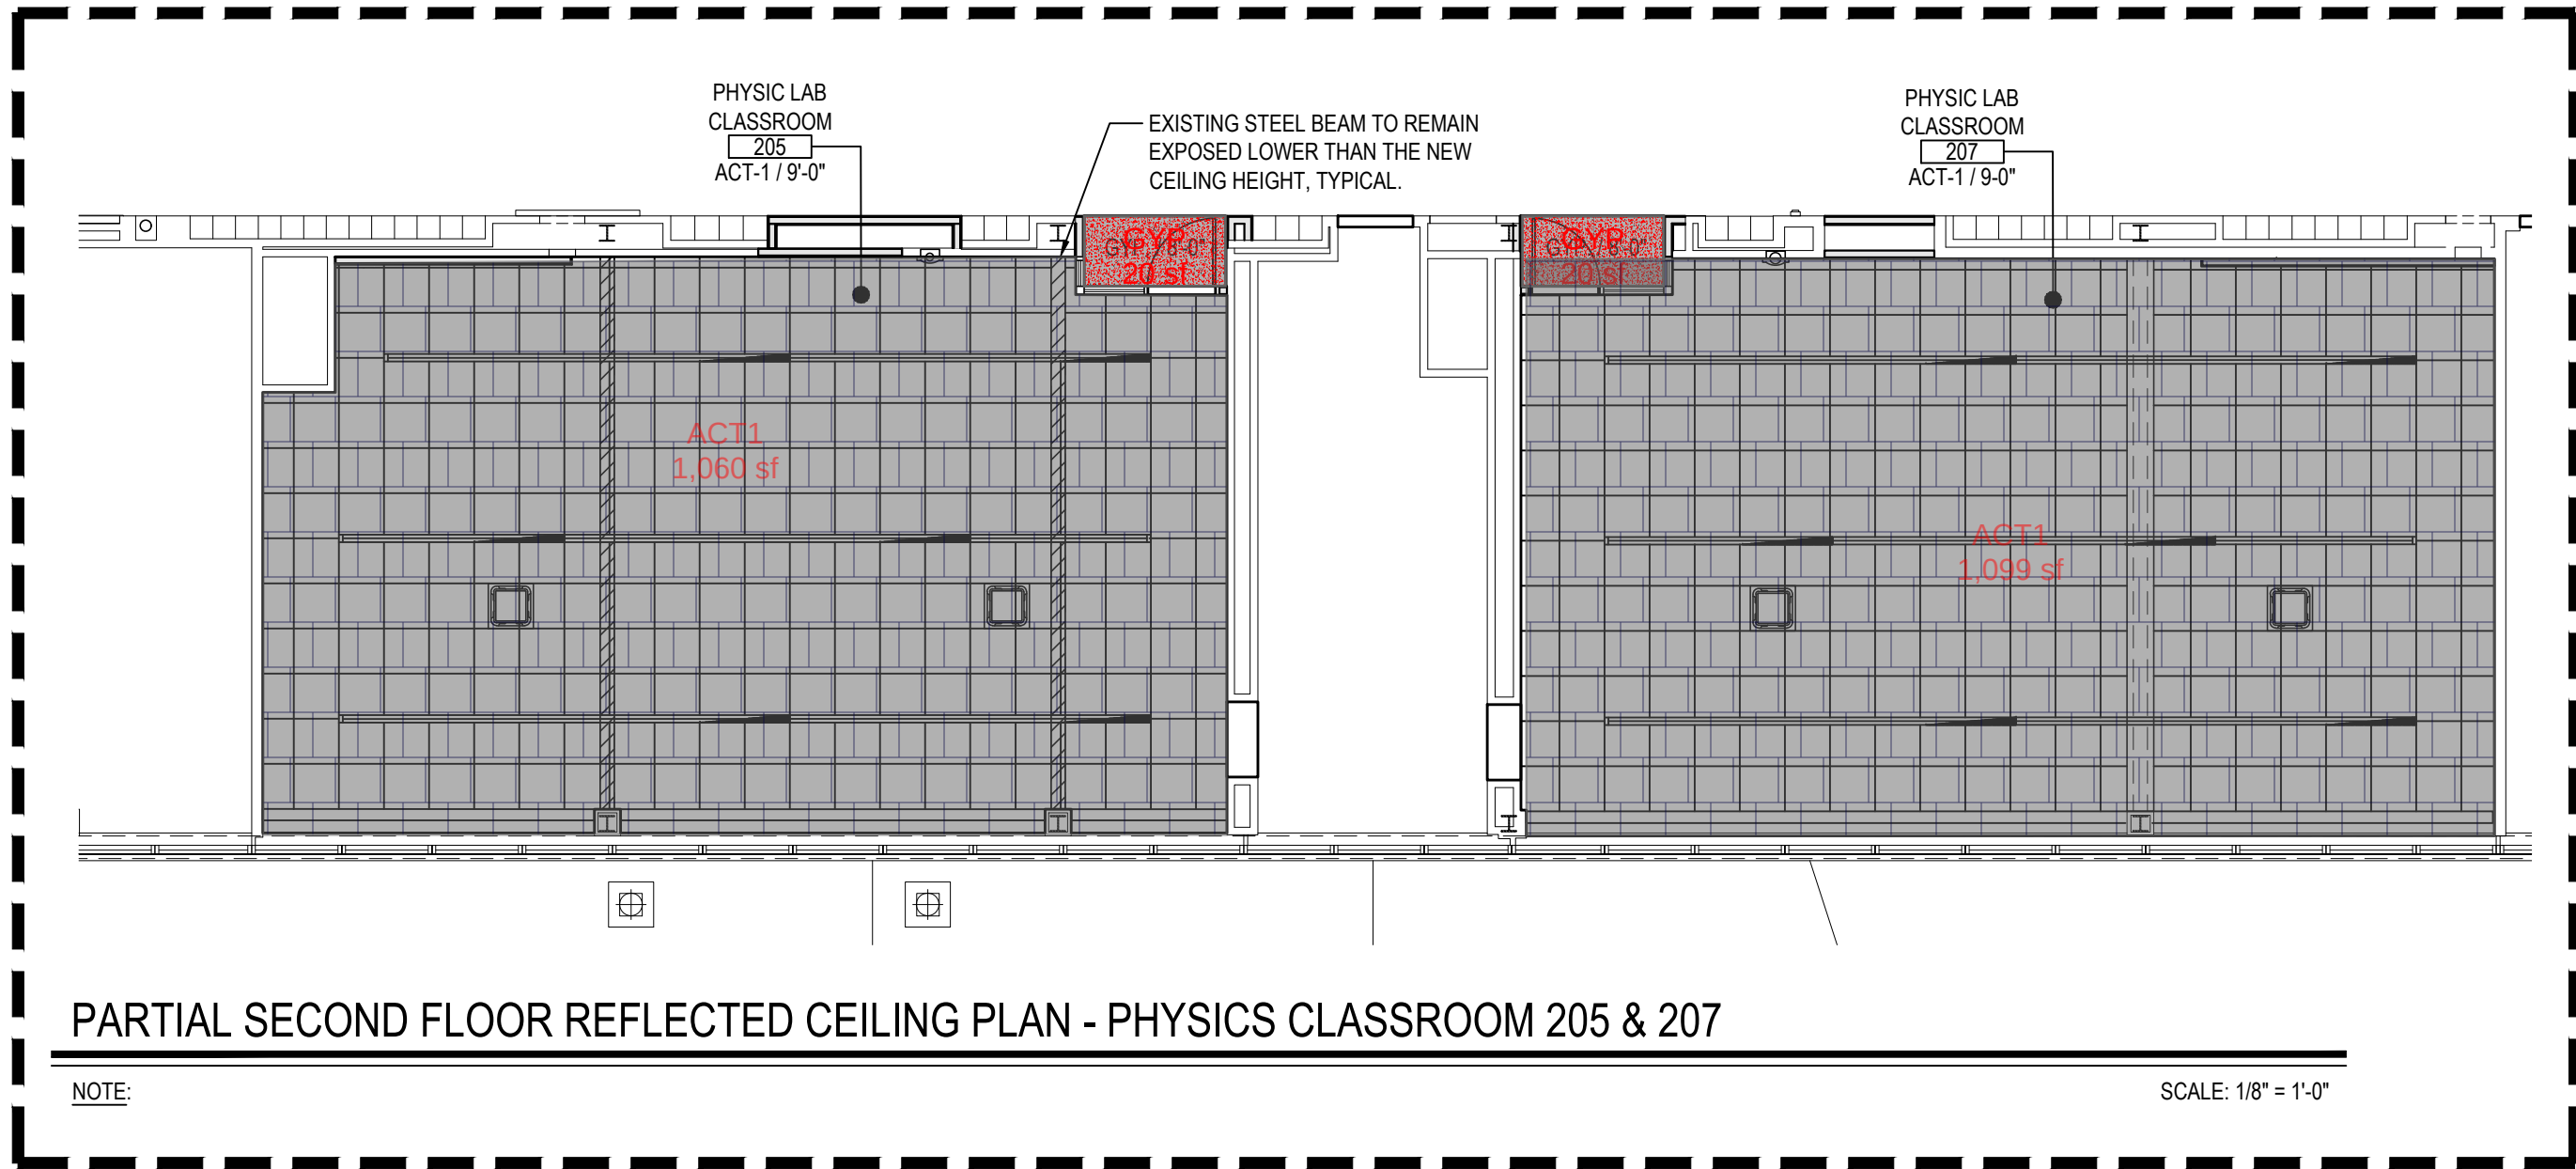

PARTIAL SECOND FLOOR REFLECTED CEILING PLAN - PHYSICS CLASSROOM 205 & 207

NOTE:

SCALE: 1/8" = 1'-0"

Second Floor

Label	Quantity	Unit
ACT1	3,390	sf
ACT2	135	sf
ACT3	255	sf
GYP	355	sf
MET1	1,211	sf

ADD ALTERNATE GC-3:
THE GENERAL CONTRACTOR SHALL STATE THE COMPLETE PRICE TO BE ADDED TO THE BASE BID TO PROVIDE ALL LABOR AND MATERIALS FOR THE DEMOLITION, AND GENERAL CONSTRUCTION WORK SCOPE REQUIRED FOR THE RECONSTRUCTION OF THE PHYSICS LABS 205 & 207 AS SHOWN ON THE DRAWINGS, AND AS SPECIFIED HEREIN.

ALL WORK SCOPE WITHIN THIS BOUNDARY SHALL BE PART OF ADD ALTERNATE GC-3

SYMBOLS LEGEND


SYMBOL	DESCRIPTION
ROOM NAME CLG. REPEAT TYPE	ROOM TAG, CEILING TILE TYPE AND FINISH CEILING ELEVATION (A.F.F.)
NO CLG.	OPEN TO STRUCTURE AND DECK ABOVE (PAINT)
	SUSPENDED ACOUSTICAL CEILING TILE AND GRID
	GYPSUM BOARD SOFFIT OVER METAL FRAMING. REFER TO DETAIL, THIS SHEET, TAPE, SPACKLE AND PAINT.
	HIGH PRESSURE LAMINATE (HPL) ARCHITECTURAL CLADDING - TRESPA 5/16" SPECTRUM UNITY PLANK. SEE A-6 SERIES DWGS FOR ADD. INFO.
	RECESSED OR SURFACE MOUNTED LIGHT FIXTURE BY E.C. REFER TO E-SERIES DRAWINGS.
	EXIT SIGN BY E.C. REFER TO E-SERIES DRAWINGS.
	CEILING MOUNTED SPEAKER BY E.C. REFER TO E-SERIES DRAWINGS.
	SMOKE / HEAT DETECTORS BY E.C. REFER TO E-SERIES DRAWINGS.
	OCCUPANCY SENSOR BY E.C. REFER TO E-SERIES DRAWINGS.
	CEILING GRILLE / REGISTER BY M.C. REFER TO M-SERIES DRAWINGS.
	NEW CASSETTE TYPE AIR CONDITIONING UNIT BY M.C. REFER TO M-SERIES DRAWINGS.
	HVAC DUCT WORK BY M.C. REFER TO M-SERIES DRAWINGS.
	NEW CORD REEL AND PLENUM BOX BY E.C. PLENUM BOX MUST BE COORDINATED WITH NEW CEILING SYSTEM AND G.C. COORDINATE BOX LOCATION WITH BUILDING STEEL. SEE DETAIL 3/E7/01 FOR ADD. INFO.
	EXTERIOR WALL MOUNTED LIGHT FIXTURE BY E.C. REFER TO E-SERIES DRAWINGS.
	CEILING MOUNTED CABINET HEATER BY M.C. REFER TO M-SERIES DRAWINGS.
	NEW SPRINKLER HEADS. REFER TO SP-SERIES DRAWINGS FOR ADD. INFO.
	REVISION CLOUD AND KEYED DESIGNATION. REFER TO DRAWING TITLE BLOCK FOR ADDITIONAL INFORMATION.

TYPICAL REFLECTED CEILING PLAN NOTES

- CEILING PLANS MAY NOT INDICATE ALL MECHANICAL AND / OR ELECTRICAL CEILING MOUNTED ITEMS. REFER TO M - SERIES AND E - SERIES DRAWINGS FOR ADDITIONAL INFORMATION.
- CEILING GRID SHALL BE ARRANGED TO BE SPACED EQUALLY IN EACH DIRECTION WITH NO TILE LESS THAN 6" UNLESS OTHERWISE REQUIRED.
- PROVIDE CEILING EXPANSION JOINT AT ALL NEW TO EXISTING INTERSECTIONS AND WHERE INDICATED ON PLANS.
- UNLESS OTHERWISE NOTED, ALL SOFFITS AND WINDOW POCKETS SHALL BE 5/2" TYPE "X" GYP. BOARD OVER 18 GA. COLD FORMED FRAMING AT 16" O.C.
- ALL AREAS NOTED AS 'OPEN' AND / OR 'NO CEILING (CLG.)' SHALL BE PAINTED - INCLUDING BUT NOT LIMITED TO DECK, STRUCTURE, DUCTWORK, ETC.)
- ACOUSTICAL CEILINGS SHALL HAVE A FLAME SPREAD OF 25 OR LESS COMPLYING WITH 'ASTM E-84'; SMOKE DEVELOPED RATING OF 50 OR LESS COMPLYING WITH PERFORMANCE REQUIREMENTS AND PHYSICAL CHARACTERISTICS OF THE SPECIFIED CEILINGS AS INDICATED IN THE REFLECTED CEILING PLAN. (ASTM E-1264)
- ACOUSTICAL CEILINGS SHALL HAVE A MINIMUM NOISE REDUCTION COEFFICIENT (NRC) RATING OF 0.65.

REV.	DATE	ITEM
01	03/20/25	BID ADD. NO. 01

NOTICE
THESE DRAWINGS ARE BASED ON CONSTRUCTION DRAWINGS NOT PREPARED BY BBS ARCHITECTS, LANDSCAPE ARCHITECTS AND ENGINEERS, P.C. AND THEREFORE, MAY NOT REPRESENT THE CONDITIONS AS CONSTRUCTED AT THE TIME. ALL EXISTING CONDITIONS SHOWN ARE REPRESENTED AS SUGGESTIVE INFORMATION AS THEY HAVE NOT BEEN BUILT AND DETAIL FOR THE ORIGINAL DOCUMENTS OR FOR THE OWNER'S INFORMATION.

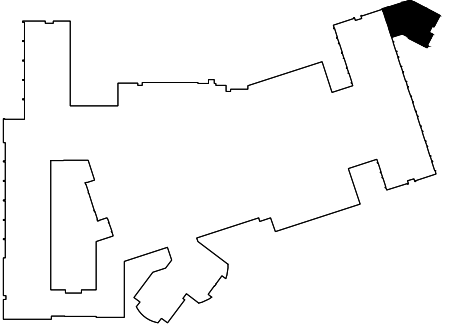

KEY PLAN

NOT TO SCALE

GARDEN CITY UNION FREE SCHOOL DISTRICT
ADDITIONS AND ALTERATIONS
GARDEN CITY HIGH SCHOOL
GARDEN CITY, NASSAU COUNTY, NEW YORK

PROJECT

DRAWING BY: WCA
CHECK BY: GWS

NOTICE

THIS DRAWING, PREPARED FOR THE SPECIFIC PROJECT INDICATED IS AN INSTRUMENT OF SERVICE, AND THE PROPERTY OF BBS ARCHITECTS, LANDSCAPE ARCHITECTS AND ENGINEERS, P.C. INFRINGEMENT OR ANY USE OF THIS DRAWING FOR ANY OTHER PROJECT IS PROHIBITED. ANY ALTERATION OR REPRODUCTION OF THIS DOCUMENT IS ALSO PROHIBITED WITHOUT THE WRITTEN CONSENT OF THE ARCHITECT OR ENGINEER.

BBS
ARCHITECTS
LANDSCAPE ARCHITECTS
ENGINEERS

244 EAST MAIN STREET | 187 WOLF ROAD, STE. 205
PATCHOGUE | ALBANY
NEW YORK 11772 | NEW YORK 12205
T: 631.475.0349 | T: 518.621.7650
F: 631.475.0361 | F: 518.621.7655

www.BBSARCHITECTURE.com

SED No.

28-02-19-03-0-007-034

DISTRICT

GARDEN CITY UNION FREE
SCHOOL DISTRICT

PROJECT

GARDEN CITY HIGH SCHOOL
ADDITIONS AND ALTERATIONS

DWG TITLE

PARTIAL SECOND FLR REFLECTED CEILING PLANS

SCALE:

AS NOTED

DATE:

MARCH 6, 2025

BID PICK-UP:

MARCH 6, 2025

FILE No:

24-145

A10.02